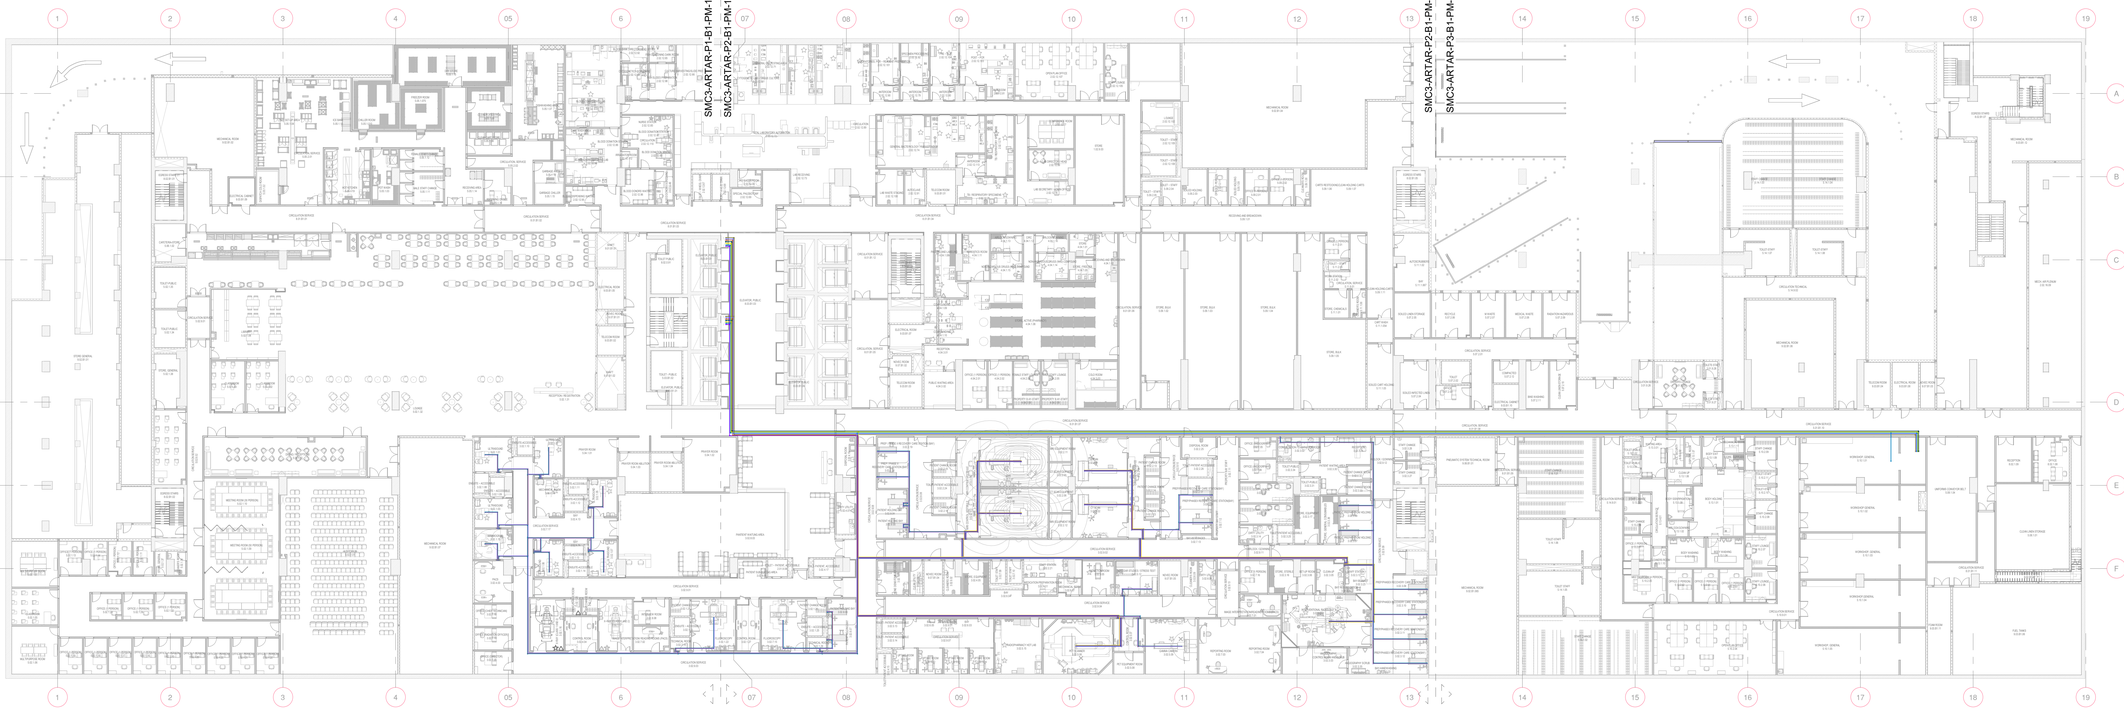


B01 BASEMENT 01 LOWER LEVEL MASTER PLAN

1 : 250

CLIENT

smc Hospital مستشفى

PROJECT CONSULTANT

ARCH.CENTRE المركز المعماري CONSULTING ENGINEERS استشارات هندسية

ALRASHID PROPERTIES الراشد العقارية

MAAP

KEY PLAN



GENERAL NOTES

1 - ANY DISCREPANCIES ARE TO BE BROUGHT TO THE ATTENTION OF THE ENGINEER AND RESOLVED PRIOR TO COMMENCEMENT OF ANY WORK.

2 - ALL DRAWINGS SHOULD BE READ IN CONJUNCTION WITH RELEVANT SECTIONS OF THE SPECIFICATIONS, SCOPE OF WORKS AND CONDITIONS OF CONTRACT. DISCREPANCIES ARE TO BE BROUGHT TO THE ATTENTION OF THE ENGINEER FOR THE FINAL ASSESSMENT.

3 - ALL THE DIMENSIONS ARE IN MILLIMETERS UNLESS NOTED OTHERWISE. ALL DIMENSIONS TO BE VERIFIED ON SITE AND APPROVED BY THE ENGINEER.

4- ALL LEVELS ON SITE PLANS ARE MEASURED BASED ON THE PROPOSED +0.00 LEVEL WHICH REFERS TO THE BENCH MARK SHOWN ON THE TOPO SURVEY PLAN SHEET NUMBER AR-020.

LEGEND

SYMBOL /ABBREVIATION	NAME
	VAC - MEDICAL GAS VACUUM PIPE
	SA7 - MEDICAL GAS SURGICAL AIR PIPE
	O2 - MEDICAL GAS OXYGEN PIPE
	MA4 - MEDICAL GAS MEDICAL AIR PIPE
	CO2 - MEDICAL GAS CARBON DIOXIDE PIPE
	AGSS - MEDICAL GAS ANAESTHETIC GAS SCAVENGING SYSTEM PIPE
	N2O - MEDICAL GAS NITROUS OXIDE PIPE
AGSSP-1	AGSS PUMP
VP-1	VACUUM COMPRESOR
CAD-1	AIR DRYER
CAT-1	AIR RECIEVER
VAP	VAPORAIZER
MAC-01	MA4 COMPRESOR
AVSU	AREA VALVE SERVICE UNIT WITH ALARM
LOX	LIQUID O2 TANK
H/L	HIGH LEVEL
L/L	LOW LEVEL
D/D	DROP DOWN
O/U	OFFSET UP
F/A	FROM ABOVE
F/B	FROM BELOW
T/A	TO ABOVE
T/B	TO BELOW
AFC	ABOVE FALSE CEILING

ARTAR COORDINATION

CHECKED	NAME	SIGNATURE	DATE
PRINCIPAL MECHANICAL ENGINEER	Eng.Yaser Al Hafiz		
PRINCIPAL MECHANICAL ENGINEER	Eng.Faras Elouah		
ELECTRO-MECHANICAL MANAGER	Eng.Mamoun Jawad		

MAAP COORDINATION

CHECKED	NAME	SIGNATURE	DATE
Operational Manager	Eng.Ola Magdy		
BIM Manager	Eng.Mohammed Hany		
Architectural & ID	Eng.Mohammed Hany		
Structure	Eng.Mahmoud Mounir		
Electrical & LC	Eng.Aly AlKaissi		
Mechanical/FF,PL	Eng.Mohammed Kamal		

RELATED DOCUMENTS, LETTERS & RFI'S REFERENCES

NO.	DOC. NO.	DOC. DESCRIPTION	REV	DATE
01	DB142-DAR-TD-B01-DWG-PM-1005M	BASEMENT 01 MEDICAL GAS MASTER PLAN	00	OCT- 2024
02	DB142-DAR-TD-B01-DWG-PM-1005P1	BASEMENT 01 MEDICAL GAS PARTIAL PLAN 1	00	OCT- 2024
03	DB142-DAR-TD-B01-DWG-PM-1005P2	BASEMENT 01 MEDICAL GAS PARTIAL PLAN 2	00	OCT- 2024
04	DB142-DAR-TD-B01-DWG-PM-1005P3	BASEMENT 01 MEDICAL GAS PARTIAL PLAN 3	00	OCT- 2024

REVISION

REV	DATE	ISSUED FOR	DRW	CHK	PM	BIMM
00	10.2026	SHOP DRAWING	AH	AK	M.K.	T

PROJECT TITLE

SPECIALIZED MEDICAL CENTER – 3 (SMC 3)

RIYADH – KSA – AL WADI DISTRICT

B01 - MAIN HOSPITAL

DISCIPLINE

MEDICAL GAS SYSTEM

SHEET TYPE

MEDICAL GAS FLOOR PLANS- BIM DRAWING LOD 350

SHEET TITLE

BASEMENT 01 LEVEL MEDICAL GASES MASTER PLAN

PROJECT NO	BLDG. NO	SHEET NO	SCALE	REV MARK
SMC3	B01	1005	1 : 250	00

DRAWING NO

SMC3-ARTAR-M-B1-PM-1005-DWG

0 50mm 100mm
(Sheet Size - ISO - A0 (841x189 mm))