
SMC3-ARTAR-P2-B2-PF-1004-DWG

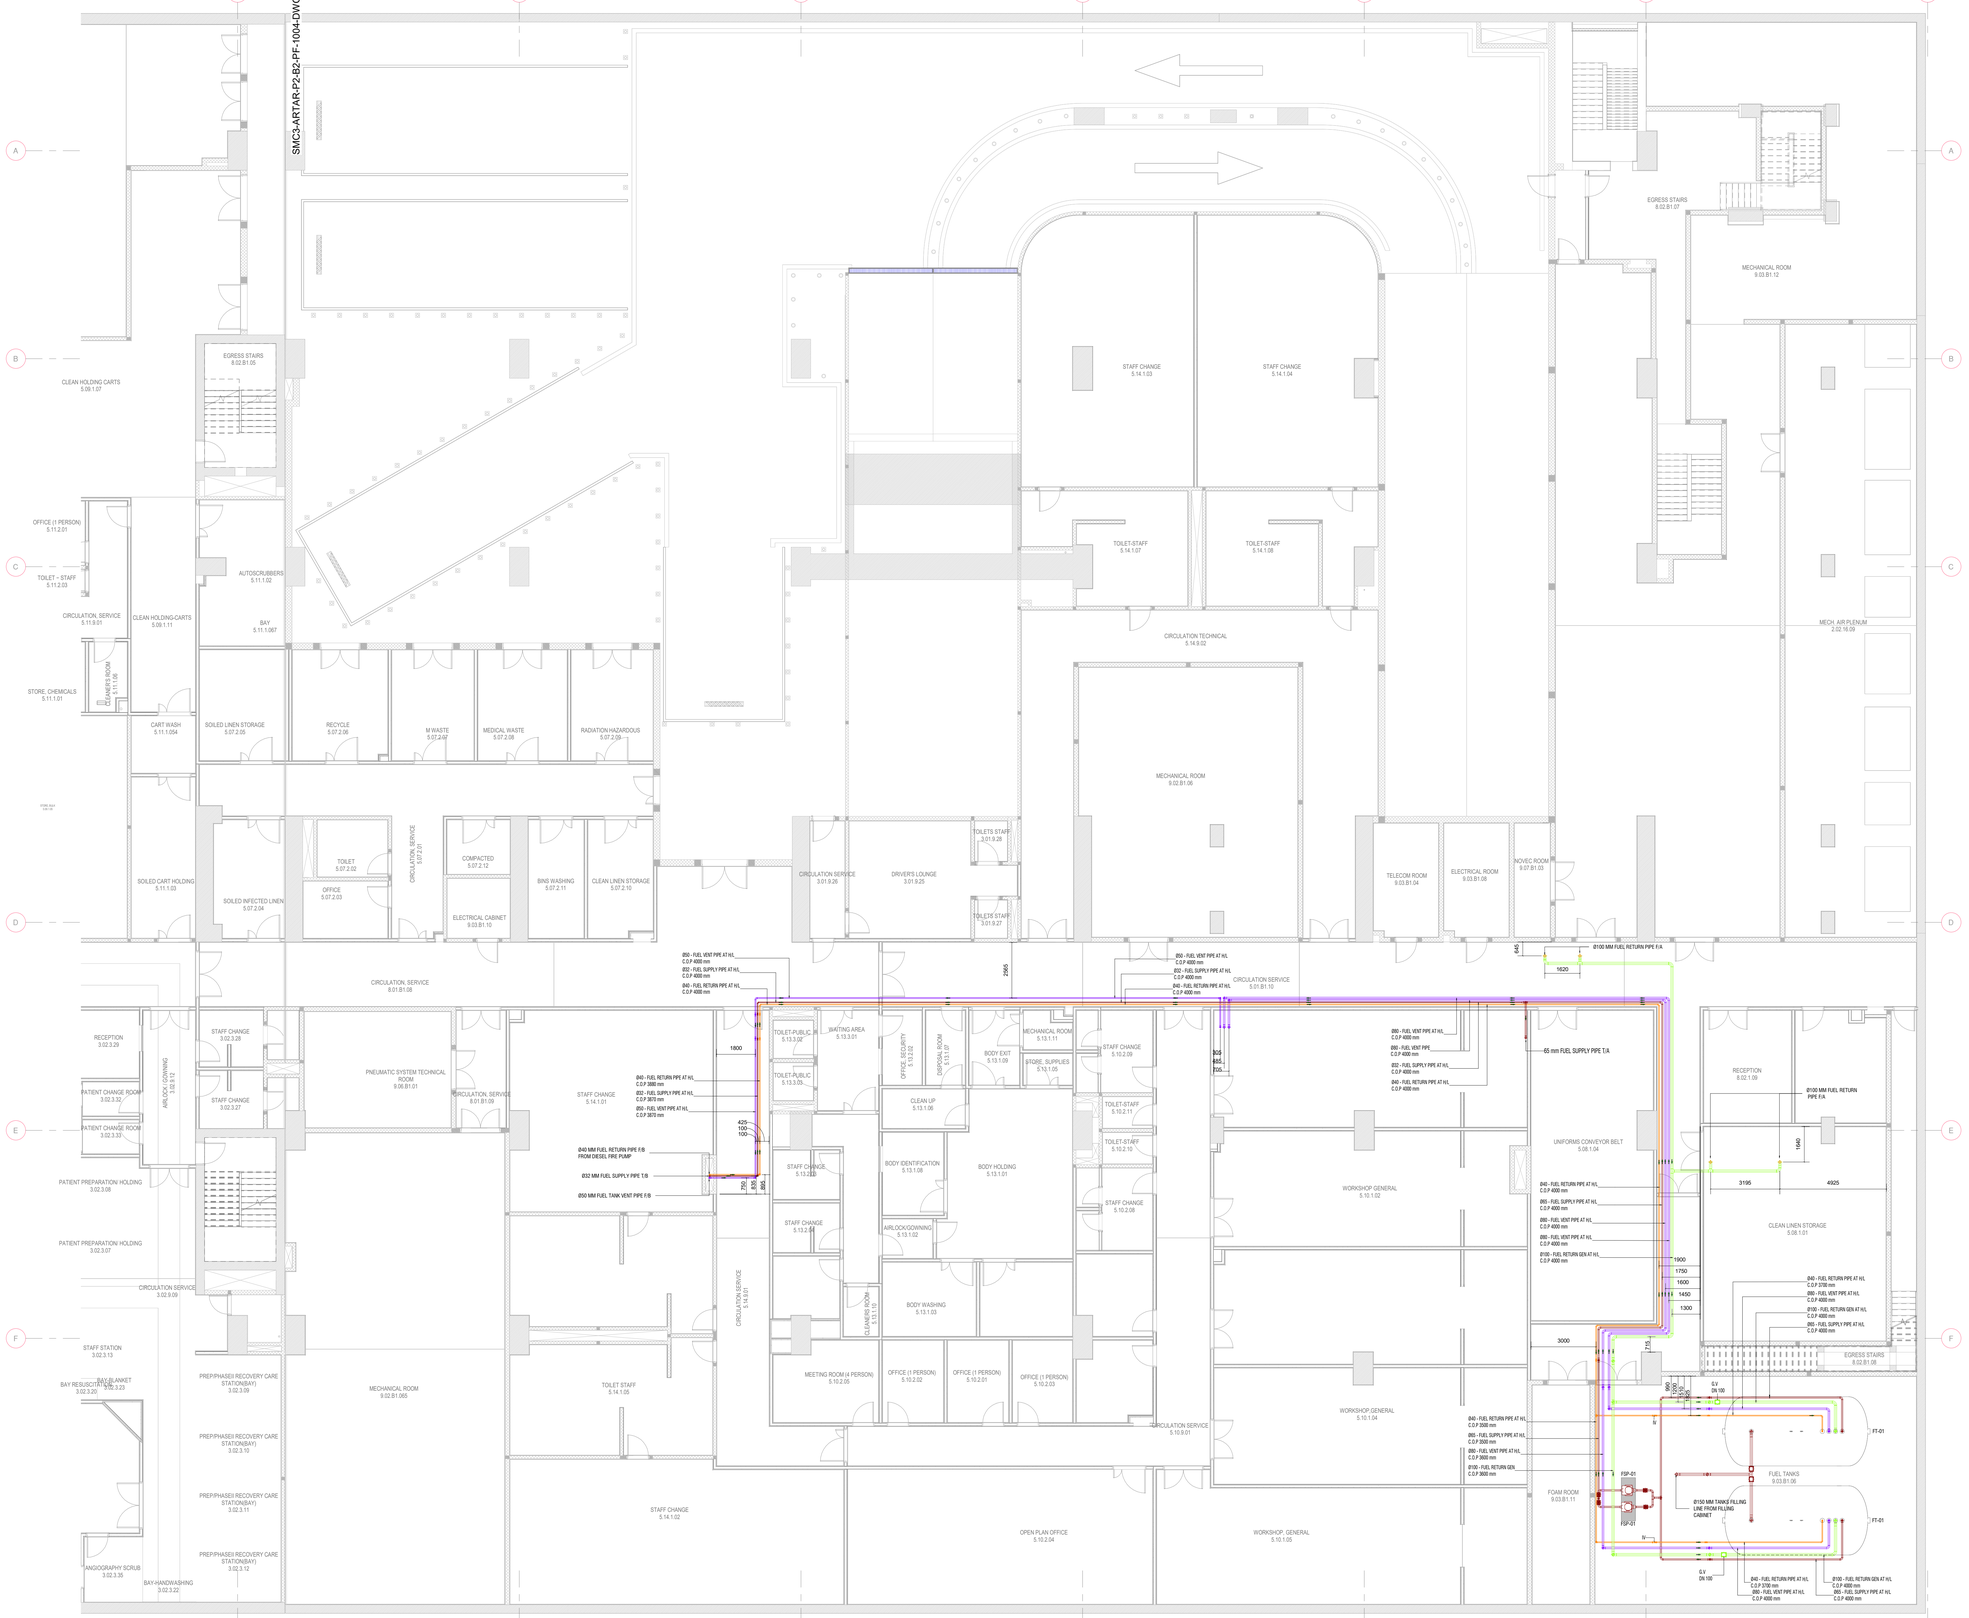


P03 BASEMENT 01 LOWER LEVEL MASTER PLAN SHEETS - PART3

1 : 100

CLIENT

PROJECT CONSULTANT

KEY PLAN

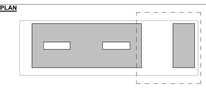

GENERAL NOTES

1 - ANY DISCREPANCIES ARE TO BE BROUGHT TO THE ATTENTION OF THE ENGINEER AND RESOLVED PRIOR TO COMMENCEMENT OF ANY WORK.

2 - ALL DRAWINGS SHOULD BE READ IN CONJUNCTION WITH RELEVANT SECTIONS OF THE SPECIFICATIONS, SCOPE OF WORKS AND CONDITIONS OF CONTRACT. DISCREPANCIES ARE TO BE BROUGHT TO THE ATTENTION OF THE ENGINEER FOR THE FINAL ASSESSMENT.

3 - ALL THE DIMENSIONS ARE IN MILLIMETERS UNLESS NOTED OTHERWISE. ALL DIMENSIONS TO BE VERIFIED ON SITE AND APPROVED BY THE ENGINEER.

4- ALL LEVELS ON SITE PLANS ARE MEASURED BASED ON THE PROPOSED +0.00 LEVEL WHICH REFERS TO THE BENCH MARK SHOWN ON THE TOPO SURVEY PLAN SHEET NUMBER AR-020.

LEGEND & ABBREVIATION

	FUEL VENT PIPE
	FUEL SUPPLY PIPE
	FUEL RETURN PIPE
FT	FUEL TANK
FSP	FUEL PUMP
FUP	FUEL PIPE
H/L	HIGH LEVEL
L/L	LOW LEVEL
D/D	DROP DOWN
O/U	OFFSET UP
F/A	FROM ABOVE
F/B	FROM BELOW
T/A	TO ABOVE
T/B	TO BELOW
AFC	ABOVE FALSE CEILING

PIPE MATERIAL

PIPE WORK	MATERIAL
UNDERGROUND FUEL PIPES	HDPE
ABOVE GROUND FUEL PIPES	BLACK STEEL, SCH0

ARTAR COORDINATION

CHECKED	NAME	SIGNATURE	DATE
PRINCIPAL MECHANICAL ENGINEER	Eng.Yaser Al Hafiz		
PRINCIPAL MECHANICAL ENGINEER	Eng.Faras Elouah		
ELECTRO-MECHANICAL MANAGER	Eng.Mamoun Jawad		

MAAP COORDINATION

CHECKED	NAME	SIGNATURE	DATE
OPERATIONAL MANAGER	Eng.Ola Magdy		
BIM MANAGER	Eng.Mohammed Hany		
ARCHITECTURAL & ID	Eng.Mohammed Hany		
STRUCTURAL	Eng.Mahmoud Mounir		
ELECTRICAL & LC	Eng.Aly AlKassi		
MECHANICAL / FF / HL	Eng.Mohammed Kamel		

RELATED DOCUMENTS, LETTERS & RFI'S REFERENCES

NO.	DOC. NO.	DOC. DESCRIPTION	REV	DATE
01	DB142-DAR-TD-B01-DWG-PF-1005M...	BASEMENT 01 LEVEL FUEL MASTER PLAN...	00	OCT - 2024
02	DB142-DAR-TD-B01-DWG-PF-1005P3...	BASEMENT 01 LEVEL FUEL PARTIAL PLAN-03	00	OCT - 2024

REVISION

REV	DATE	ISSUED FOR	DRW	CHK	PM	BIMM
00	10.2026	SHOPDRAWING	A.H	A.K	A.F	T

PROJECT TITLE

SPECIALIZED MEDICAL CENTER – 3 (SMC 3)

RIYADH – KSA – AL WADI DISTRICT

B01 - MAIN HOSPITAL

DISCIPLINE: FUEL SYSTEM

SHEET TYPE: FUEL SYSTEM PLANS
BIM DRAWING-LOD 350

SHEET TITLE: BASEMENT 01 LEVEL FUEL PARTIAL PLAN- PART3

PROJECT NO	BLDG. NO	SHEET NO	SCALE	REV MARK
SMC3	B01	1005	1 : 100	00

DRAWING NO: SMC3-ARTAR-P3-B1-PF-1005-DWG

Sheet size: ISO - A0 (841x189 mm) 0mm 100mm