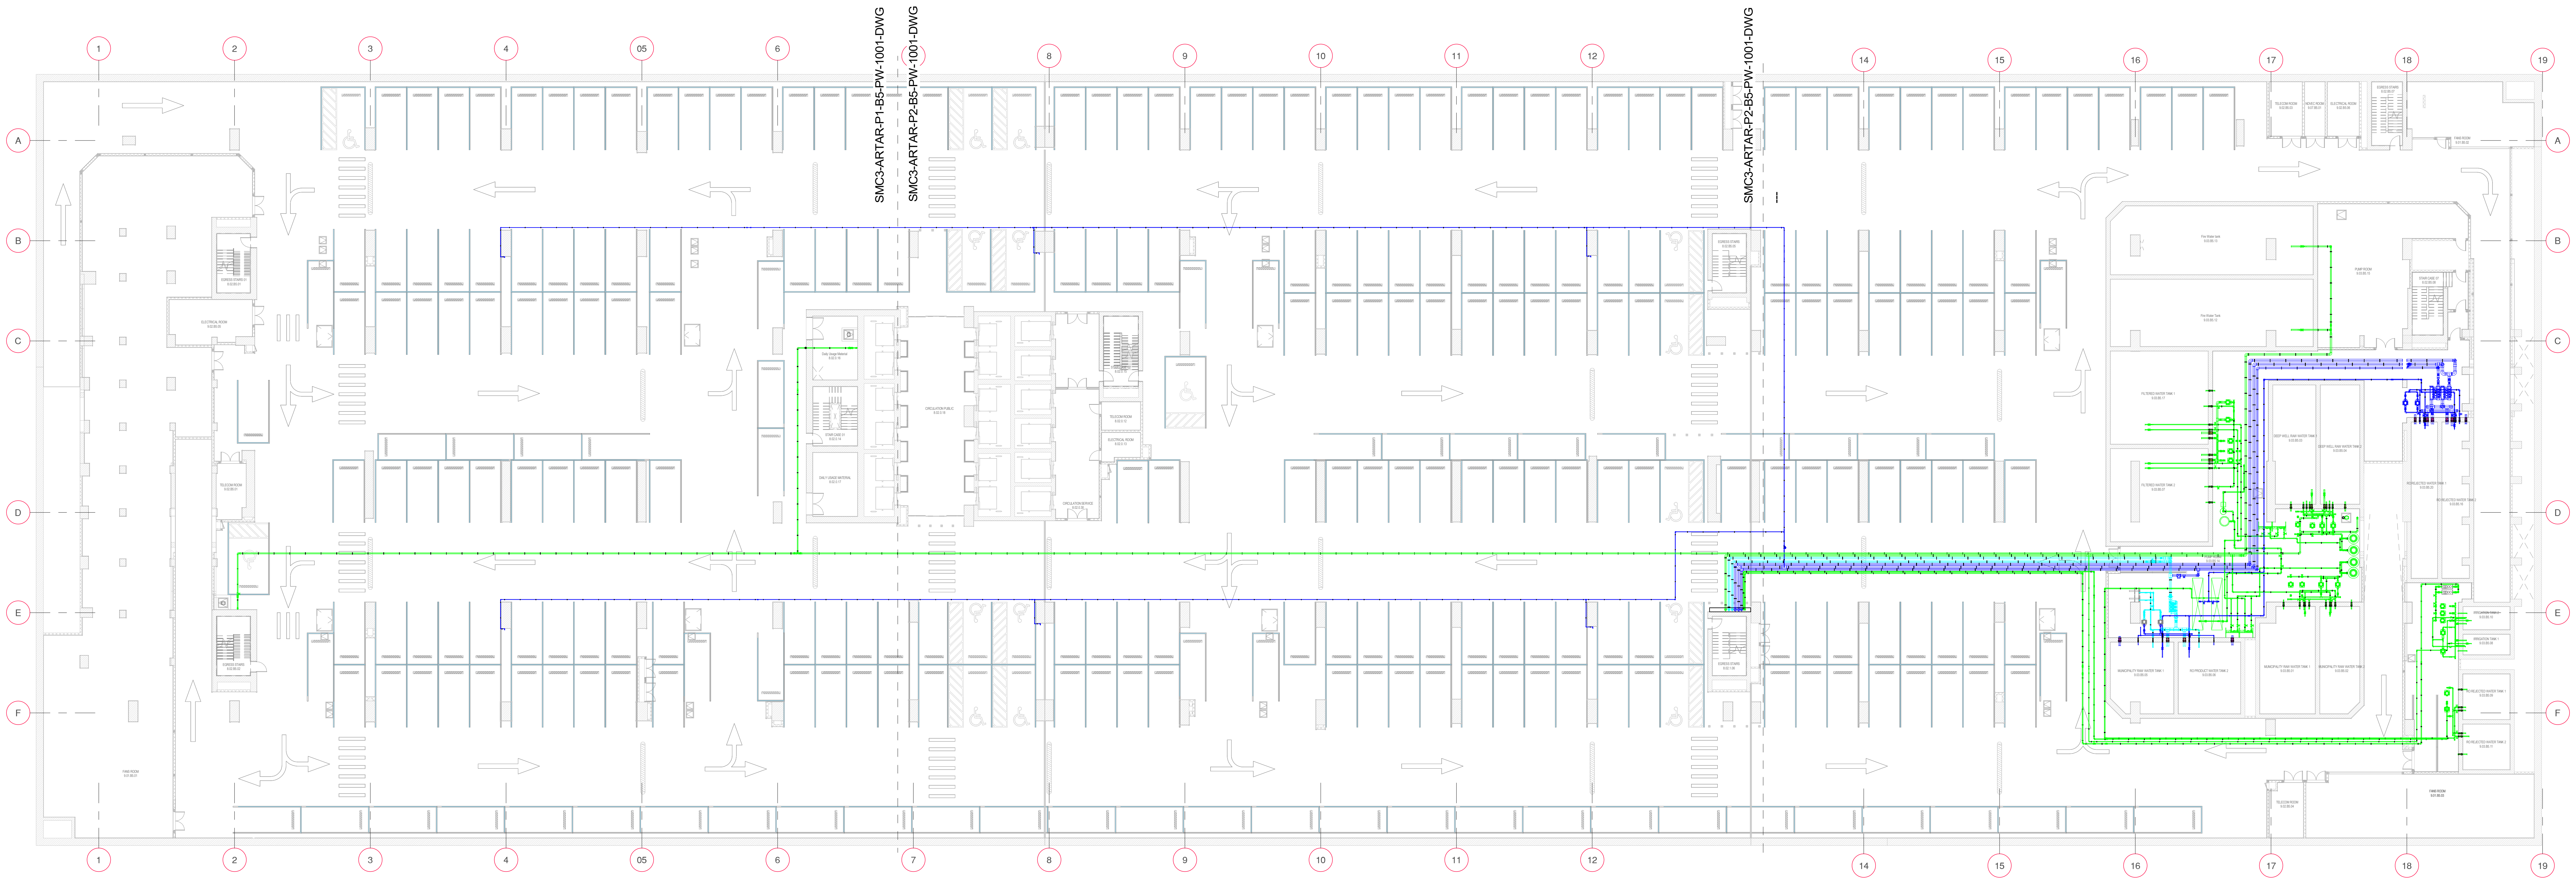
SMC3-ARTAR-P1-B5-PW-1001-DWG
SMC3-ARTAR-P2-B5-PW-1001-DWG
SMC3-ARTAR-P2-B5-PW-1001-DWG
FANS ROOM
9.01.B5.01
1
2
3
4
05
6
7
8
9
10
11
12
14
15
16
17
18
19
A
B
C
D
E
F

B05

BASEMENT 05 HIGHER LEVEL MASTER PLAN

1 : 250

CLIENT

smc Hospital مستشفى

PROJECT CONSULTANT

المركز المعماري ARCH.CENTRE CONSULTING ENGINEERS استشارات هندسية SINCE 1977

الراشد العقارية ALRASHID PROPERTIES

MAAP
Website:www.maapeg.com
Info@maapeg.com
Mobile: +201100607556
Landline: +20225657001
Address: St.17, New Cairo, Cairo, Egypt

KEY PLAN

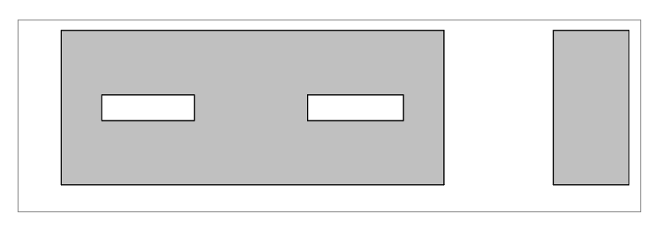

GENERAL NOTES

-ALL DIMENSION IN MM.
- ALL PIPE SIZE SHOWN ARE NOMINAL PIPE DIAMETER IN MILLIMETERS.
- ALL MATERIAL ARE ACCORDING TO APPROVED MATERIAL SUBMITTAL.
- ALL FIXTURES SHALL BE PROVIDED WITH P OR S TRAP.

LEGEND

SYMBOL	DESRIBTION
≡	DOMESTIC COLD WATER PIPE (DCWP)
≡	HOT WATER PIPE (HWP)
≡	HOT WATER RETURN PIPE (HWRP)
≡	NON POTABLE TREATED WATER PIPE (NPTEP)
≡	RO PRODUCT WATER PIPE (RPWP)
	GATE VALVE (G.V)
	CHECK VALVE (C.V)
	BALL VALVE (B.V)
	HOSE BIB (H.B)
	BALANCING VALVE (BC.V)
	PRESSURE REDUCING VALVE
	FLOATING VALVE (F.V)

T/A	TO ABOVE
F/A	FROM ABOVE
T/B	TO BELOW
T/B	FROM BELOW
H/L	HIGH LEVEL
M/L	MIDDLE LEVEL
L/L	LOW LEVEL
U/G	UNDER GROUND
U/T	UNDER TILES
DN	DOWN
BP	BOOSTER PUMP
FITP	FILTER TRANSFER PUMP
ROTP	RO TRANSFER PUMP
CP	CIRCULATION PUMP
LP	LIFTING PUMP
IRR	IRRIGATION PUMP
WFP	WATER FRATURE PUMP
BHP	BORE HOLE PUMP
MMF	WATER MULTIMEDIA FILTER
CUSIO	COPPER - SILVER IONIZER UNIT
RO	RO UNIT
HP	HEAT PUMP
HWST	HOT WATER STORAGE CALORIFER
HEX	PALTE HEAT EXCHANGER

PIPE MATERIAL	
PIPE WORK	MATERIAL
COLD WATER FOR TOILETS FLUSHING	PPR-PN16
RO COOLED COLD WATER	PPR-PN10
HOT WATER SUPPLY & RETURN	PPR-PN16

ARTAR COORDINATION

CHECKED	NAME	SIGNATURE	DATE
PRINCIPAL MECHANICAL ENGINEER	Eng.Yaser Al Hafiz		
PRINCIPAL MECHANICAL ENGINEER	Eng.Freas Eloush		
ELECTRO-MECHANICAL MANAGER	Eng.MAmoun Jawad		

MAAP COORDINATION

CHECKED	NAME	SIGNATURE	DATE
Operational Manager	Eng.Ola Magdy	Ola Magdi	
BIM Manager	Eng.Mohammed Hany	Mohammed Hany	
Architectural & ID	Eng.Mohammed Hany	Mohammed Hany	
Structure	Eng.Mahmoud Mounir		
Electrical & LC	Eng.Aly AlKazaz	Aly Alkazaz	
Mechanical/FF/PL	Eng.Mohammed Kamal	M.kamal	

RELATED DOCUMENTS, LETTERS & RFI'S REFERENCES

NO.	DOC. NO.	DOC. DESCRIPTION	REV	DATE
01	DB142-DAR-TD-B1-DWG-PW-1001M	BASEMENT 05 LEVEL WATER SUPPLY MASTER PLAN	00	OCT - 2024
02	DB142-DAR-TD-B1-DWG-PW-1001P1	BASEMENT 05 LEVEL WATER SUPPLY PARTIAL PLAN-01	00	OCT - 2024
03	DB142-DAR-TD-B1-DWG-PW-1001P2	BASEMENT 05 LEVEL WATER SUPPLY PARTIAL PLAN-02	00	OCT - 2024
04	DB142-DAR-TD-B1-DWG-PW-1001P3	BASEMENT 05 LEVEL WATER SUPPLY PARTIAL PLAN-03	00	OCT - 2024
05	DB142-DAR-TD-B1-DWG-PE-6010	DOMESTIC WATER PUMP ROOM	00	OCT - 2024

REVISION

REV	DATE	ISSUED FOR	DRW	CHK	PM	BIMM
00	10.2026	SHOPDRAWING	Z.Q	A.K	A.F	1

PROJECT TITLE

SPECIALIZED MEDICAL CENTER – 3 (SMC 3)

RIYADH – KSA – AL WADI DISTRICT

B01 - MAIN HOSPITAL

DISCIPLINE
WATER SUPPLY SYSTEM

SHEET TYPE
WATER SUPPLY PLANS - BIM DRAWING - LOD 350

SHEET TITLE
BASEMENT 05 LEVEL WATER SUPPLY MASTER PLAN

PROJECT NO	BLDG. NO	SHEET NO	SCALE	REV MARK
SMC3	B01	1001	1:250	00

DRAWING NO
SMC3-ARTAR-M-B5-PW-1001-DWG

Sheet size - ISO A0 (841x1189 mm)
50mm
100mm