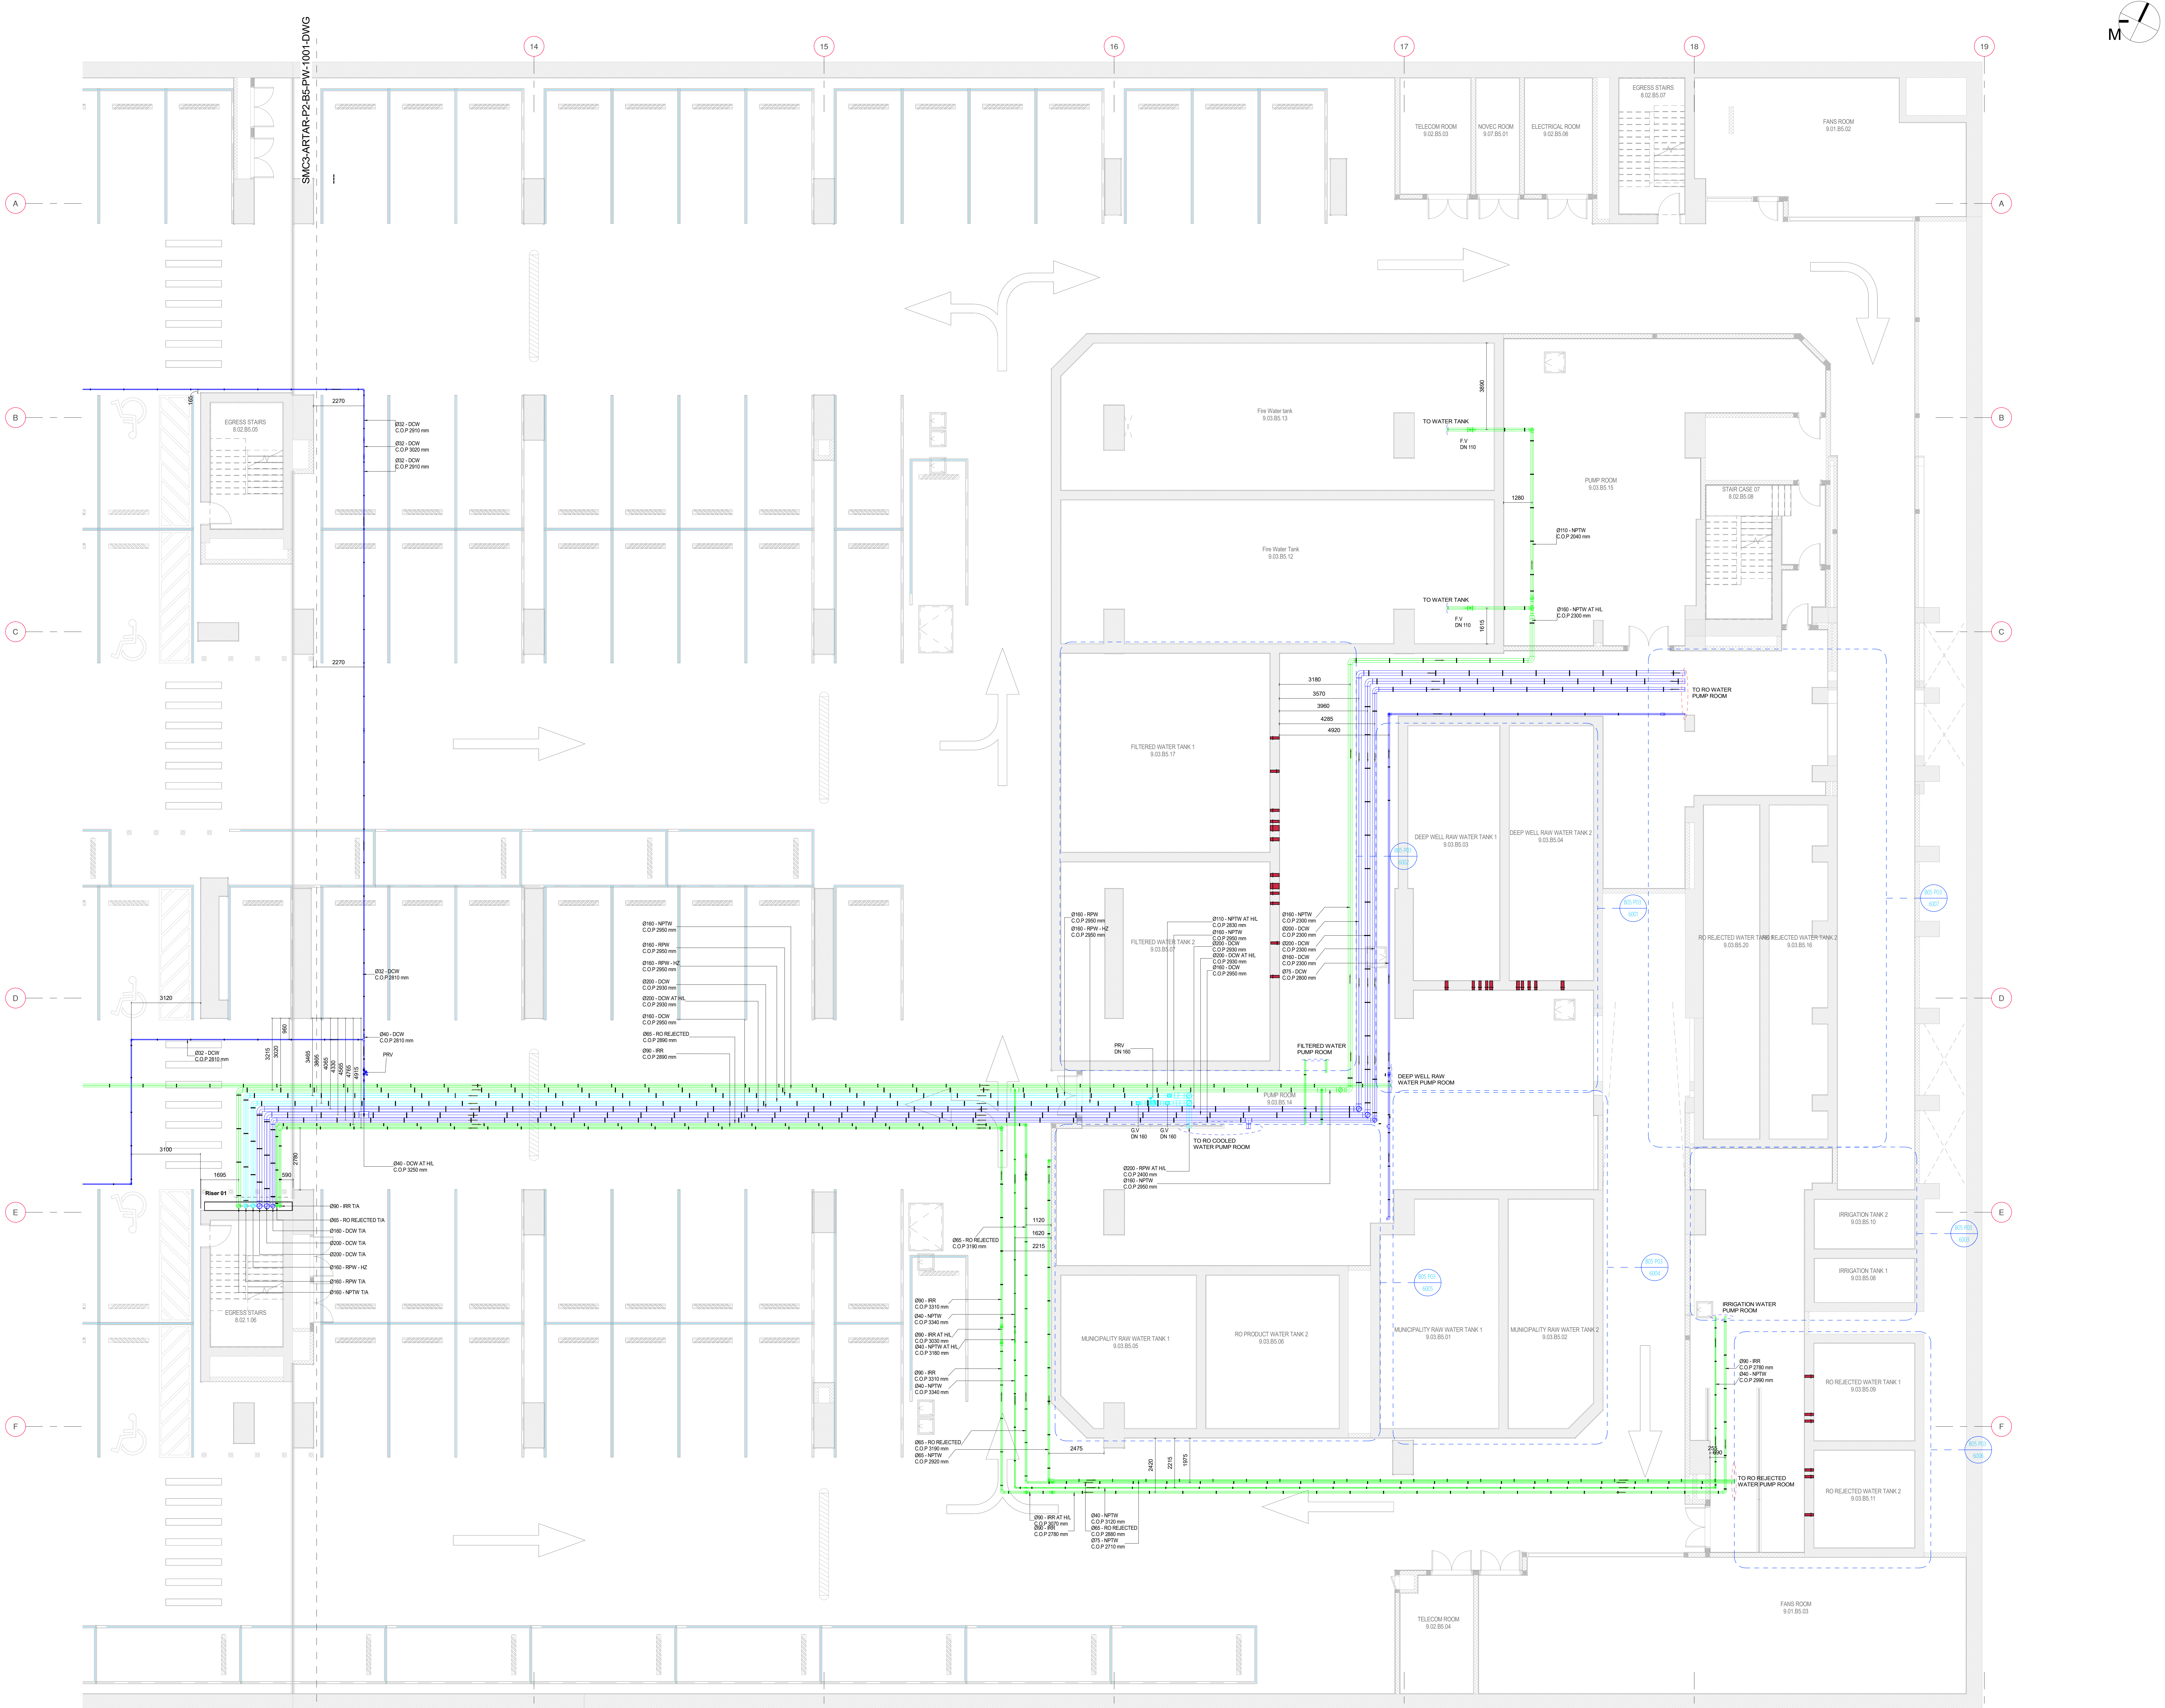

B05
P03

BASEMENT 05 HIGHER LEVEL PART 3 NEW

1 : 100

Sheet size - ISO A0 (841x1189 mm)

0

50mm

100mm

**CLIENT**

smc Hospital مستشفى

**PROJECT CONSULTANT**

ARCH.CENTRE المركز المعماري
SINCE 1977
CONSULTING ENGINEERS استشارات هندسية

الراشد العقارية
ALRASHID PROPERTIES

MAAP
Website:www.maapeg.com
Info@maapeg.com
Mobile: +201100607556
Landline: +20225657001
Address: St.17, New Cairo, Cairo, Egypt

**KEY PLAN**

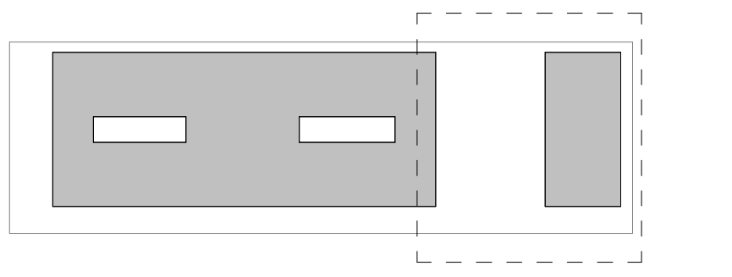

## GENERAL NOTES

-ALL DIMENSION IN MM.
- ALL PIPE SIZE SHOWN ARE NOMINAL PIPE DIAMETER IN MILLIMETERS.
- ALL MATERIAL ARE ACCORDING TO APPROVED MATERIAL SUBMITTAL.
- ALL FIXTURES SHALL BE PROVIDED WITH P OR S TRAP.

## LEGEND

| SYMBOL | DESRIBTION |
|---|---|
| ═ | DOMESTIC COLD WATER PIPE (DCWP) |
| ═ | HOT WATER PIPE (HWP) |
| ═ | HOT WATER RETURN PIPE (HWRP) |
| ═ | NON POTABLE TREATED WATER PIPE (NPTEP) |
| ═ | RO PRODUCT WATER PIPE (RPWP) |
|  | GATE VALVE (G.V) |
|  | CHECK VALVE (C.V) |
|  | BALL VALVE (B.V) |
|  | HOSE BIB (H.B) |
|  | BALANCING VALVE (BC.V) |
|  | PRESSURE REDUCING VALVE |
|  | FLOATING VALVE (F.V) |

|  |  |
|---|---|
| T/A | TO ABOVE |
| F/A | FROM ABOVE |
| T/B | TO BELOW |
| T/B | FROM BELOW |
| H/L | HIGH LEVEL |
| M/L | MIDDLE LEVEL |
| L/L | LOW LEVEL |
| U/G | UNDER GROUND |
| U/T | UNDER TILES |
| DN | DOWN |
| BP | BOOSTER PUMP |
| FITP | FILTER TRANSFER PUMP |
| ROTP | RO TRANSFER PUMP |
| CP | CIRCULATION PUMP |
| LP | LIFTING PUMP |
| IRR | IRRIGATION PUMP |
| WFP | WATER FRATURE PUMP |
| BHP | BORE HOLE PUMP |
| MMF | WATER MULTIMEDIA FILTER |
| CUSIO | COPPER - SILVER IONIZER UNIT |
| RO | RO UNIT |
| HP | HEAT PUMP |
| HWST | HOT WATER STORAGE CALORIFER |
| HEX | PALTE HEAT EXCHANGER |

| PIPE MATERIAL |  |
|---|---|
| PIPE WORK | MATERIAL |
| COLD WATER FOR TOILETS FLUSHING | PPR-PN16 |
| RO COOLED COLD WATER | PPR-PN10 |
| HOT WATER SUPPLY & RETURN | PPR-PN16 |

**ARTAR COORDINATION**

| CHECKED | NAME | SIGNATURE | DATE |
|---|---|---|---|
| PRINCIPAL MECHANICAL ENGINEER | Eng.Yaser Al Hafiz |  |  |
| PRINCIPAL MECHANICAL ENGINEER | Eng.Freas Eloush |  |  |
| ELECTRO-MECHANICAL MANAGER | Eng.MAmoun Jawad |  |  |

**MAAP COORDINATION**

| CHECKED | NAME | SIGNATURE | DATE |
|---|---|---|---|
| Operational Manager | Eng.Ola Magdy | Ola Magdi |  |
| BIM Manager | Eng.Mohammed Hany | Mohammed Hany |  |
| Architectural & ID | Eng.Mohammed Hany | Mohammed Hany |  |
| Structure | Eng.Mahmoud Mounir |  |  |
| Electrical & LC | Eng.Aly AlKazaz | Aly Alkazaz |  |
| Mechanical/FF/PL | Eng.Mohammed Kamal | M.kamal |  |

## RELATED DOCUMENTS, LETTERS & RFI'S REFERENCES

| NO. | DOC. NO. | DOC. DESCRIPTION | REV | DATE |
|---|---|---|---|---|
| 01 | DB142-DAR-TD-B1-DWG-PW-1001M | BASEMENT 05 LEVEL WATER SUPPLY MASTER PLAN | 00 | OCT - 2024 |
| 02 | DB142-DAR-TD-B1-DWG-PW-1001P1 | BASEMENT 05 LEVEL WATER SUPPLY PARTIAL PLAN-01 | 00 | OCT - 2024 |
| 03 | DB142-DAR-TD-B1-DWG-PW-1001P2 | BASEMENT 05 LEVEL WATER SUPPLY PARTIAL PLAN-02 | 00 | OCT - 2024 |
| 04 | DB142-DAR-TD-B1-DWG-PW-1001P3 | BASEMENT 05 LEVEL WATER SUPPLY PARTIAL PLAN-03 | 00 | OCT - 2024 |
| 05 | DB142-DAR-TD-B1-DWG-PE-6010 | DOMESTIC WATER PUMP ROOM | 00 | OCT - 2024 |

**REVISION**

| REV | DATE | ISSUED FOR | DRW | CHK | PM | BIMM |
|---|---|---|---|---|---|---|
| 00 | 10.2026 | SHOPDRAWING | Z.Q | A.K | A.F | 1 |

**PROJECT TITLE**

SPECIALIZED MEDICAL CENTER – 3 (SMC 3)

RIYADH – KSA – AL WADI DISTRICT

B01 - MAIN HOSPITAL

**DISCIPLINE**
WATER SUPPLY SYSTEM

**SHEET TYPE**
WATER SUPPLY PLANS - BIM DRAWING - LOD 350

**SHEET TITLE**
BASEMENT 05 LEVEL WATER SUPPLY PARTIAL PLAN-03

| PROJECT NO | BLDG. NO | SHEET NO | SCALE | REV MARK |
|---|---|---|---|---|
| SMC3 | B01 | 1001 | 1:100 | 00 |

**DRAWING NO**
SMC3-ARTAR-P3-B5-PW-1001-DWG